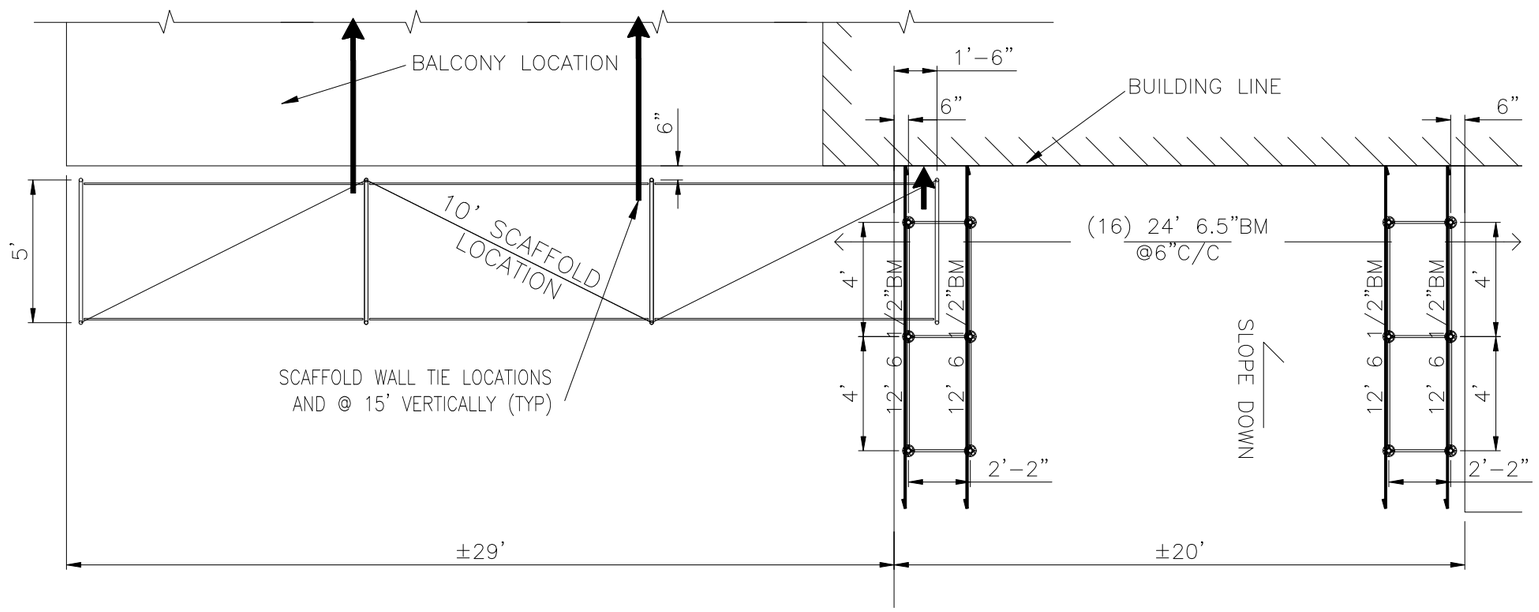

SCAFFOLDING LAYOUT PLAN

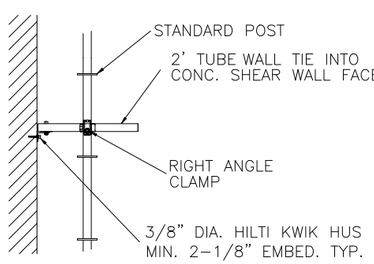

DETAIL A

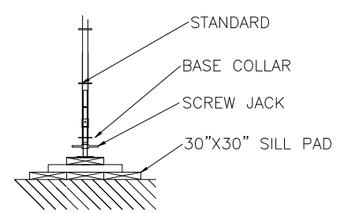

DETAIL B

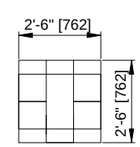

NOTES:
1. TIES @14' (MAX) HORIZONTALLY
2. TIES @15' (MAX) VERTICALLY
3. $\frac{3}{8}$"x4" ANCHOR BOLTS
4. TOTAL DESIGN LOAD: 50psf

NOTES:
CONTAINMENT – WORKING SCAFFOLD PLATFORM PERIMETER IS PROTECTED WITH KICKPLATE.

CONTAINMENT – SCAFFOLD PERIMETER IS COVERED WITH 60% WING-PIERCING DEBRIS NETTING.

CONTAINMENT – SCAFFOLD PERIMETER IS COVERED WITH SOLID TARPING AND/OR HOARDING

TIES-INS – AL TUBE C/W BOLTED STEEL ANGLE, CLAMPED TO STD. POST, AND FASTENED TO CONCRETE WITH ONE (1)HILTI KWIK HUS-EZ I CARBON STEEL SCREW ANCHOR, $\frac{1}{4}$" DIA., MIN. 2.5" EMBEDMENT, ALLOWABLE TENSTION LOAD 1340 LB / 6.0 kN (25000PSI CONC.), SHEAR 755 LB/3.4 kN

NOTES:
1. VERIFY ALL DIMENSIONS SHOWN ON THE STRUCTURAL DRAWINGS PRIOR TO CONSTRUCTIONS AND IMMEDIATELY NOTIFY THE DEISGN ENGINEER OF ANY DISCREPANCY.
2. DO NOT SCALE DRAWINGS
3. SAFEGUARD ALL EXISTING STRUCTURES AFFECTED BY THIS CONSTRUCTION. PREFORM A PRE-CONSTRUCTION SURVEY OF THE CONSTRUCTION SITE. EXAMINE AND NOTE THE CONDITION OF EXISTING ADJACENT STRUCTURES BEFORE AND DURING CONSTRUCTION.
4. ALL SCAFFOLDING IS TO BE ERECTED PLUMB AND LEVEL AND IN ACCORDANCE WITH C.S.A. CODE S.269.1 "FALSEWORK FOR CONSTRUCTION PURPOSES".
5. CO-ORDINATE WITH ALL OTHER TRADES WHERE SUCH TRADES AFFECT THE STRUCTURE.
6. L&A SCAFFOLD IS RESPONSIBLE FOR THE DESIGN, INSTALLATION, AND SCAFFOLD IN THE SCOPE OF THE DRAWINGS.
7. FOLLOW ALL MANUFACTURER'S SPECIFICATIONS.

COMPONENTS:
RINGLOCK SYSTEM SCAFFOLD – ETOBICOKE IRON WORKS OR EQUIVALENT DSS,SCAFOM. MAX ALLOWABLE LEG LOAD 2/ 2M VERTICAL BRACING 5000LBS. CONNECTIONS 2500LBS.
TUBES – 1.5" DIA. SCH. 40 ALUMINUM TUBE (1.9" OD X 0.145" WALL)
CLAMPS – RIGHT ANGLE / SWIVEL SLIP LOAD 25000 LBS. SAFE WORK LOAD – RIGHT ANGLE CLAMP 2500 LBS & SWIVEL SWL 1500 LBS (PIN SHEAR)
CRIBBING/SILL PADS – AS SHOWN
DECKING/PLATFORMS – ALUMINUM RAIL, PLYWOOD TOP PLATFORMS MAX ALLOWABLE LOADING 75 PSF. LAMINATED WOOD SCAFFOLD PLANKS (LP LVL OR EQUIVALENT) 74 PSF @ MAX. 10'9" SIMPLE SPAN. $\frac{3}{4}$" PLYWOOD MAX SPAN 19". $\frac{5}{8}$ PLYWOOD MAX SPAN 16"

	:{{¦95 Chw/hb{ew¦/t:hb	oc!!twlomoc
w9±	59{/w:t:hb	5!69

w9±:{:hb{

ENGINEER'S SEAL

V. H. BHACHECH Member 34648 PROFESSIONAL ENGINEER
2025-07-25

APEGM Certificate of Authorization Virag H. Bhachech No. 5224 Date: 2025-07-25

THIS DRAWING HAS BEEN PREPARED FROM AND BASED ON THE FOLLOWING INFORMATION SUPPLIED TO US BY OR ON BEHALF OF THE CUSTOMER.

HI hwLD:b hC 5w! ² :bDº
OI C! - Iº
MI 5w! ² :bD bhº
PI 5!695º

THE CONTRACTOR SHALL CHECK AND VERIFY ALL DIMENSIONS AND REPORT ALL ERRORS AND OMMISIONS TO THE DESIGN PROFESSIONAL WHOSE SEAL IS AFFIXED TO THIS DRAWING. DO NOT SCALE THE DRAWINGS.

©HI-LITE SYSTEMS LTD. THIS DRAWING IS THE EXCLUSIVE PROPERTY OF HI-LITE SYSTEMS. NO UNAUTHORIZED USE, COPY OR DISCLOSURE IS TO BE MADE WITHOUT THE PERMISSION FROM HI-LITE SYSTEMS.

HI-LITE
ALUMINUM SHORING SYSTEMS

ПРСТ а ¦ðÌá wÑ¦Т а¦áàÌáàÌáèàÌ¦ hb!/ly¦ÌÑ¦!Т [c/ w¢ϕ
¢Šª хмсγтγγγрмпо λ C¦Šª хмсγтγγγрсро

9¡γ¦ª KÌÌÌŠ ɤ K¡γ¦ÌÌŠ¡ÁÁÁÁÌŠ γ¦ÌÌŠ²Y

² Šϕ ¡¦ÌŠª ϕϕϕ¦KÌγ¦ÌÌŠ¡ÁÁÁÁÌŠ γ¦ÌÌŠ²Y

ɤ Ɪu[¢9 {_ ¢9a{ [¢5
¢¡¦ 5w! ² :bD:¢ Ɪ19 ª:/[:¢8 hwhC:bwt_ hC Ɪu[¢9 {_ ¢9a{ [¢5
bh !b!¢Ɪbw¢b5 :[¢:/hC, hw 5L/!h[:w9:{ ¢h .9 a!59 ² ¢Ɪ¢h[:¢ Ɪ29 ² w¢¢b t:bw a:[[:hb C:wh a Ɪu[¢9 {_ ¢9a{ [¢5

twhw9/¢ b! a9

HCCM ² !w59

² lbblt9DT a.

/¦{¢h a9w

[ƻ! {/!CCh[5lbD

5w! ² :bD ¢:¢[9

{/!CCh[5lbD [!¸h¦¢

{/![9

bɤ¢ɤ{ɤ

5w! ² b	/I9/Y95	5!¢9
{ɤ	±ɤ.ɤλɤ5ɤ	нмλɤ¦bλомос

kh. bh	5w! ² :bD bh	w9±:{:hb
[!{Kϕx	[!{KϕxϱCн	мм